


WINDOW NOTES:

1. OPERABLE WINDOWS SHALL BE PROVIDED WITH SUBSTANTIAL LOCKING DEVICE.
2. WINDOWS WITHIN 40" OF THE LOCK SIDE OF A DOOR SHALL BE FULLY TEMPERED.
3. GLAZED OPENINGS WITHIN 18" OF THE FLOOR SHALL BE FULLY TEMPERED.


WINDOW SCHEDULE						
WINDOW NUMBER	TYPE	SIZE		MATERIAL	U-FACTOR	GLAZING NOTES
		WIDTH	HEIGHT			
101	A	4'-0"	3'-0"	VINYL	0.3	TEMPERED GLAZING
102	B	2'-0"	4'-0"	VINYL	0.3	TEMPERED GLAZING
103	B	2'-0"	4'-0"	VINYL	0.3	TEMPERED GLAZING
104	A	5'-0"	5'-0"	VINYL	0.3	TEMPERED GLAZING
105	B	2'-0"	2'-0"	VINYL	0.3	TEMPERED GLAZING

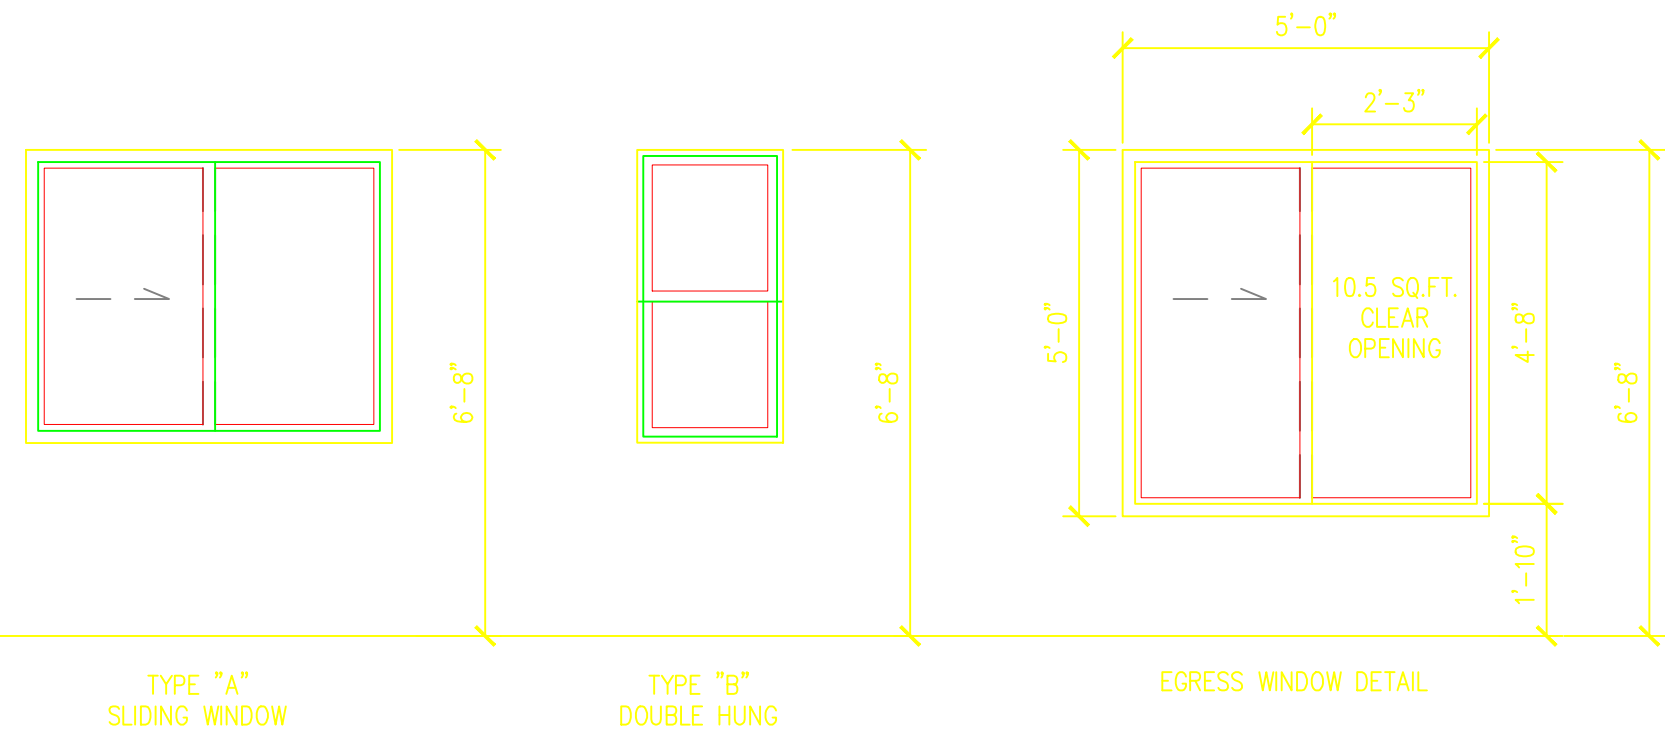

DOOR NOTES:

1. ALL JAMB / STOPS OF IN-SWINGING DOORS SHALL BE OF ONE PIECE CONSTRUCTION.
2. ALL HINGES ACCESSIBLE FROM THE OUTSIDE SHALL HAVE NON-REMOVABLE PINS.
3. ALL EXTERIOR DOORS SHALL BE 1-3/4" THICK.
4. ALL GLASS IN DOORS SHALL BE FULLY TEMPERED.
5. THE STRIKE PLATE FOR DEAD BOLTS OR MORTISE LOCKS SHALL BE SECURED TO THE JAMB AND FRAMING WITH MIN 2-1/2" LONG #10 SCREWS. DEAD BOLTS SHALL BE MINIMUM 1" THROW AND 3/8" EMBEDMENT AND SHALL CONTAIN HARDENED INSERTS.
6. LOCKS SHALL BE KEY OPERATED ON THE OUTSIDE AND REQUIRE NO KEY OR SPECIAL EFFORT ON THE INSIDE. CYLINDERS SHALL HAVE TAMPER RESISTANT ROTATING GUARDS ON THE OUTSIDE.

DOOR SCHEDULE						
DOOR NUMBER	TYPE	SIZE		FRAME / MATERIAL	GLAZING	NOTES
		WIDTH	HEIGHT			
101	A	3'-0"	6'-8"	WD	N/A	
102	A	2'-8"	6'-8"	WD	N/A	
103	A	2'-8"	6'-8"	WD	N/A	

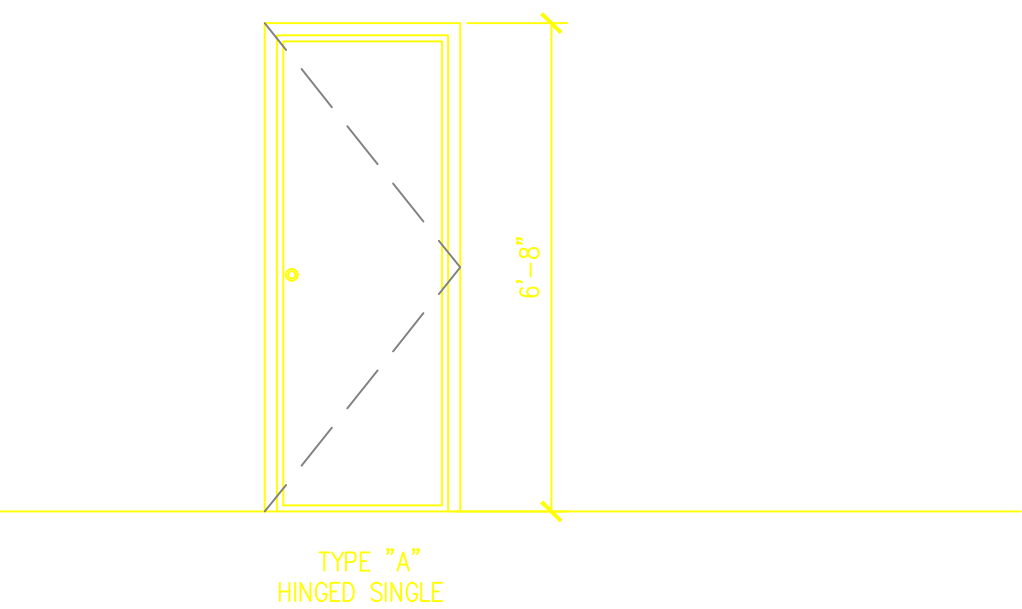

NATURAL VENTILATION IN HABITABLE ROOMS CALCULATIONS:

BEDROOM:

BEDROOM AREA IS 102 SQ.FT.
102X4% = 10.2 SQ.FT.
THE BEDROOM WINDOW CLEAR OPENING AREA IS 10.5 SQ.FT.
THEREFORE 10.5 > 10.2 SQ.FT. (4% OF THE FLOOR AREA) ==> OK

LIVING AREA:

LIVING AREA =118 SQ.FT.
118 X4% = 4.72 SQ.FT.
LIVING AREA VENTILATION= 7.8 SQ.FT. (3.9 X 2 WINDOWS CLEAR OPENING) + 18 SQ.FT. (DOOR OPENING) = 25.8 SQ.FT.
THEREFORE 25.8 > 4.72 (4% OF THE FLOOR AREA) ==> OK

KITCHEN AREA:

KITCHEN AREA =67 SQ.FT.
67X4% = 2.68 SQ.FT.
KITCHEN AREA WINDOW CLEAR OPENING IS = 6 SQ.FT.
THEREFORE 6SQ.FT.> 2.68 (4% OF THE FLOOR AREA) ==> OK

- GENERAL NOTES:
1. CONTRACTOR SHALL VERIFY ALL EXISTING CONDITION AND DIMENSIONS BEFORE ORDERING ANY MATERIALS
2. CONTRACTOR SHALL PROVIDE PROPER SHORING BEFORE ANY DEMOLITION
3. ALL PLANS ARE USED FOR CITY PERMIT ONLY AND SHALL NOT BE USED FOR CONSTRUCTION UNLESS PERMIT IS ISSUED

PLAN NOTES:

- DOUBLE CAST IRON SINK WITH GARBAGE DISPOSAL SINK FAUCET 2.2 GPM
- REFRIGERATOR SPACE, 39" CLEAR, PROVIDE WATER STUB FOR ICE MAKER
- ELECTRIC COOK TOP AND 30" METAL HOOD WITH LIGHT AND EXHAUST FAN, VENT TO OUTSIDE AIR (VERIFY DIMENSIONS WITH THE MANUFACTURER'S SPECS)
- COUNTER TOP
- BUILT-IN DISHWASHER (VERIFY DIMENSIONS WITH THE MANUFACTURER'S SPECS)
- MIRROR (FOR SIZE, SEE PLAN)
- LAVATORY
- WATER CLOSET 1.28 GPF OVER WATER RESISTANT GYP. BD.
- 30" X 60" X 70" HIGH ONE PIECE FIBER GLASS TUB/SHOWER OVER WONDERBOARD BASE W/ ANTI-SCALDING NON-SLIP JOINT HEAD 2.5 GPM. W/ PRESS. BALANCE VALVE
- INTERIOR FINISH W/ MAX. FLAME SPREAD OF CLASS III EXCEPT KITCHEN AND BATHROOM.
- SINGLE POLE AND SHELF AT WARDROBE
- MINI SPLIT
- WASHING MACHINE SPACE PROVIDE WASTE WATER AND OUTLET BOX BY TECH SPECIALTIES FAUCET 2.2 GPM
- SMITTY PAN W/ DRAIN AT WASHER
- DRYER VENT PER C.M.C. 504/ 4" DIA., 14' LONG MAX. W/ 2 ELBOWS MAX. WITH BACK-DRAFT DAMPER
- DRYER SPACE WITH 4" DIA. (14' MAX.) VENT TO OUTSIDE AIR W/ BACKDRAFT DAMPER

NOTES:

1. ALL NEWLY CONSTRUCTED BUILDINGS SHALL BE ALL-ELECTRIC BUILDINGS PER ORDINANCE NO. 187714.
- EXCEPTIONS:
- A. APPLICATION FOR A BUILDING PERMIT IS SUBMITTED, ACCEPTED BY THE DEPARTMENT OF BUILDING AND SAFETY, AND BUILDING PERMIT APPLICATION FEES ARE PAID PRIOR TO APRIL 1, 2023.
- B. APPLICATION FOR A BUILDING PERMIT FOR AN AFFORDABLE HOUSING PROJECT, AS DEFINED IN THE MAYOR'S EXECUTIVE DIRECTIVE 13, IS SUBMITTED, ACCEPTED BY THE DEPARTMENT OF BUILDING AND SAFETY, AND BUILDING PERMIT APPLICATION FEES ARE PAID PRIOR TO JUNE 1, 2023.
- C. ATTACHED ACCESSORY DWELLING UNITS USING EXISTING GAS PIPING SYSTEMS IN CONJUNCTION WITH THE PRIMARY DWELLING. D. COOKING EQUIPMENT CONTAINED WITHIN KITCHENS LOCATED IN A PUBLIC USE AREA, AS DEFINED IN THE CALIFORNIA BUILDING CODE CHAPTER 2, SUCH AS RESTAURANTS, COMMISSARIES, CAFETERIAS, AND COMMUNITY KITCHENS PROVIDED THE ELECTRICAL INFRASTRUCTURE IS INSTALLED IN ACCORDANCE WITH SECTION 99.04.106.8.1.
- E. GAS-POWERED EMERGENCY LIFE-SAFETY SYSTEMS, INCLUDING EMERGENCY BACKUP.
2. THE CONSTRUCTION SHALL NOT RESTRICT A FIVE-FOOT CLEAR AND UNOBSTRUCTED ACCESS TO ANY WATER OR POWER DISTRIBUTION FACILITIES (POWER POLES, PULL-BOXES, TRANSFORMERS, VAULTS, PUMPS, VALVES, METERS, APPURTENANCES, ETC.) OR TO THE LOCATION OF THE HOOK-UP. THE CONSTRUCTION SHALL NOT BE WITHIN TEN FEET OF ANY POWER LINES-WHETHER OR NOT THE LINES ARE LOCATED ON THE PROPERTY. FAILURE TO COMPLY MAY CAUSE CONSTRUCTION DELAYS AND/OR ADDITIONAL EXPENSES.
3. AN APPROVED SEISMIC GAS SHUT OFF VALVE OR EXCESS FLOW SHUT OFF VALVE WILL BE INSTALLED ON THE FUEL GAS LINE ON THE DOWN-STREAM SIDE OF THE UTILITY METER AND BE RIGIDLY CONNECTED TO THE EXTERIOR OF THE BUILDING OR STRUCTURE CONTAINING THE FUEL GAS PIPING. (PER ORDINANCE 170,158 AND 180,670) SEPARATE PLUMBING PERMIT IS REQUIRED.
4. PROVIDE ULTRA-FLUSH WATER CLOSETS FOR ALL NEW CONSTRUCTION. EXISTING SHOWER HEADS AND TOILETS MUST BE ADAPTED FOR LOW WATER CONSUMPTION.
5. PROVIDE (70) (72) INCH HIGH NON-ABSORBENT WALL ADJACENT TO SHOWER AND APPROVED SHATTER-RESISTANT MATERIALS FOR SHOWER ENCLOSURE. (1210.2.3, 2406.4.5, R307.2, R308.4.)
6. WATER HEATER MUST BE STRAPPED TO WALL. (507.3 & LAPC).
7. SPRINKLER SYSTEM MUST BE APPROVED BY THE MECHANICAL DIVISION PRIOR TO INSTALLATION.
8. A FIRE ALARM (VISUAL AND AUDIBLE) SYSTEM IS REQUIRED. THE ALARM SYSTEM MUST BE APPROVED BY THE FIRE DEPARTMENT AND ELECTRICAL PLAN CHECK PRIOR TO INSTALLATION. (LAMC 57.122).
9. CARBON MONOXIDE ALARM IS REQUIRED. (915.4, R315).

PROPOSED FLOOR PLAN
3/8" = 1'-0"

LEGEND:

- NEW 2X6 EXTERIOR STUD WALL
- NEW 2X4 INTERIOR STUD WALL

NOTE:
ALL DIMENSIONS ARE TAKEN FROM FACE OF STUD UNLESS NOTED OTHERWISE