




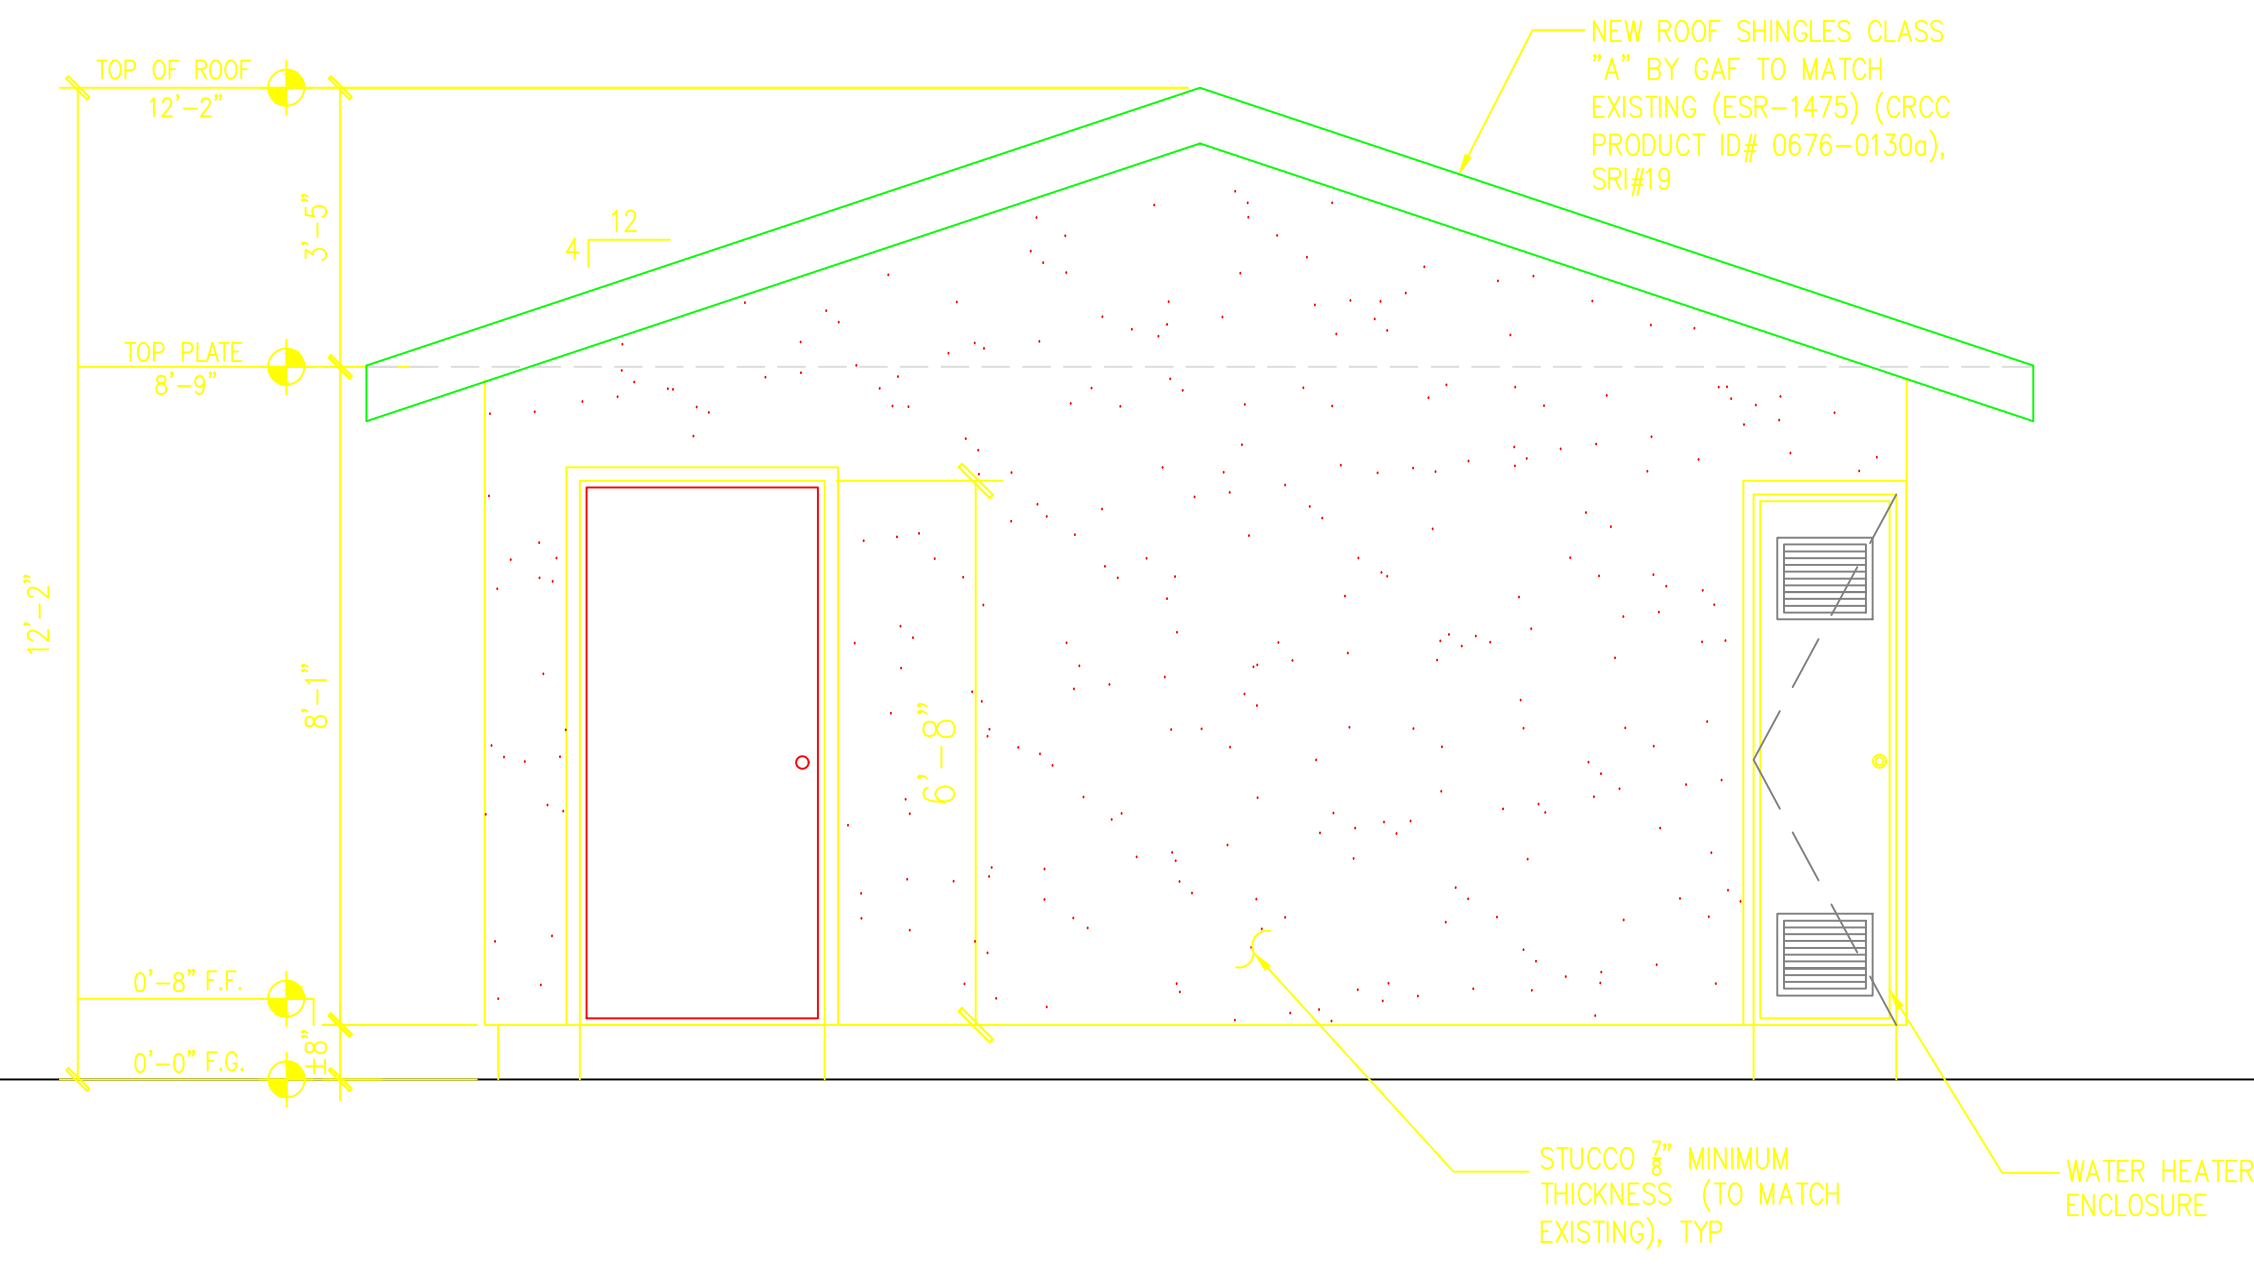


PROPOSED SOUTH ELEVATION
3/8 = 1'-0"

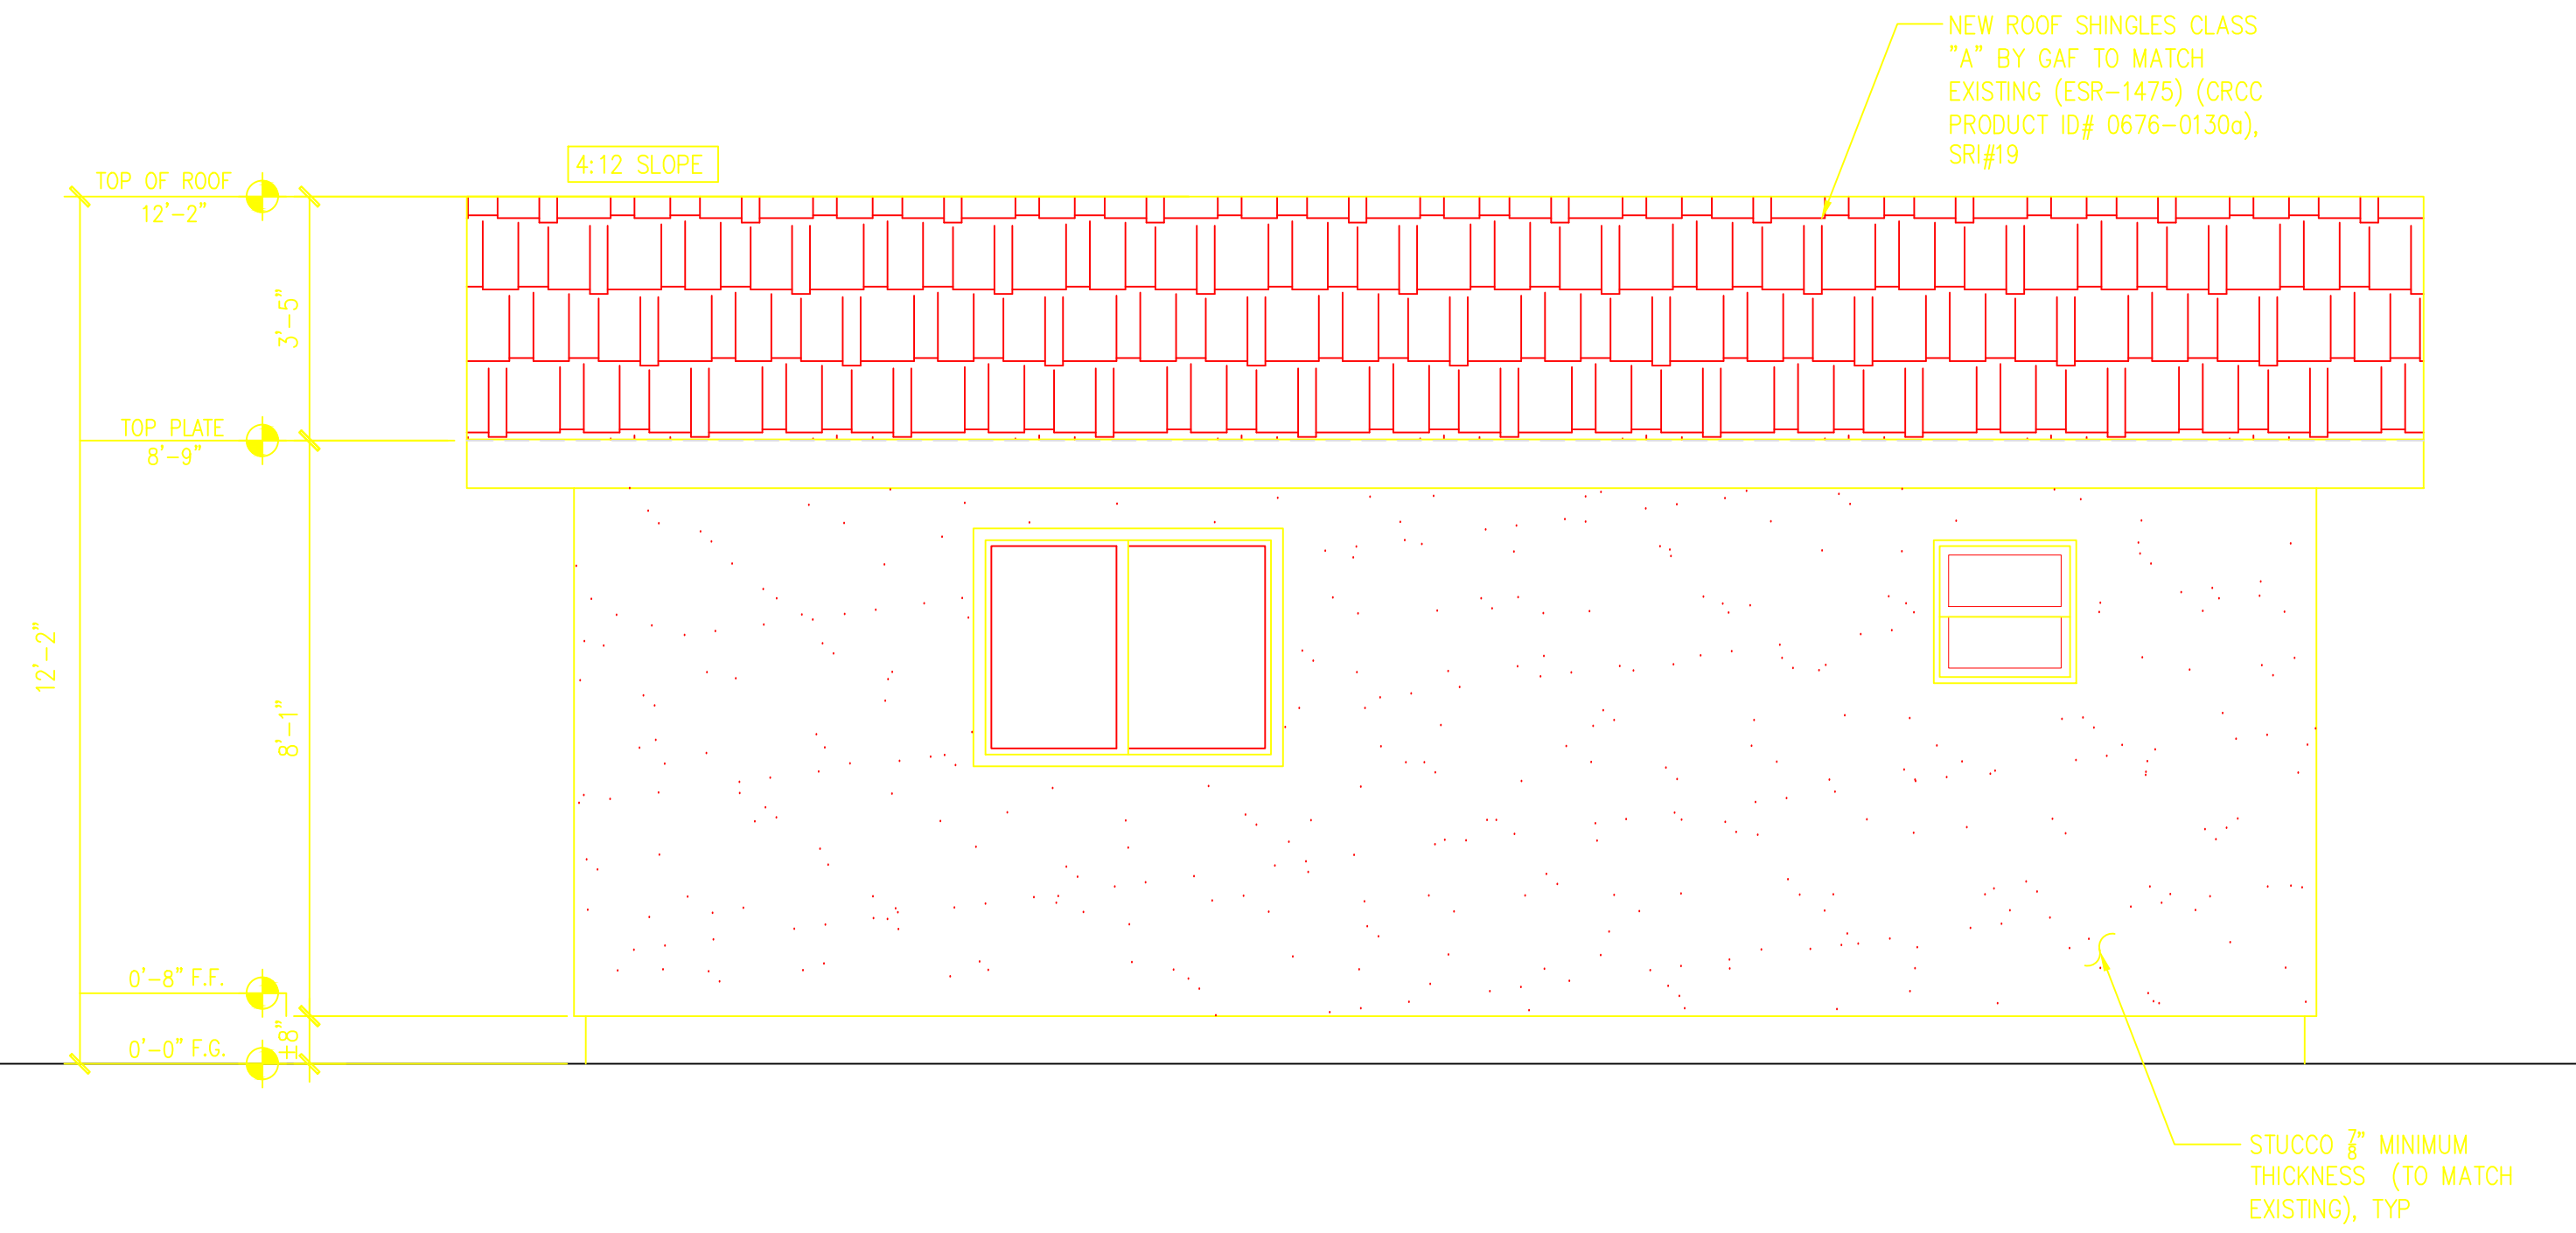

PROPOSED EAST ELEVATION
3/8 = 1'-0"

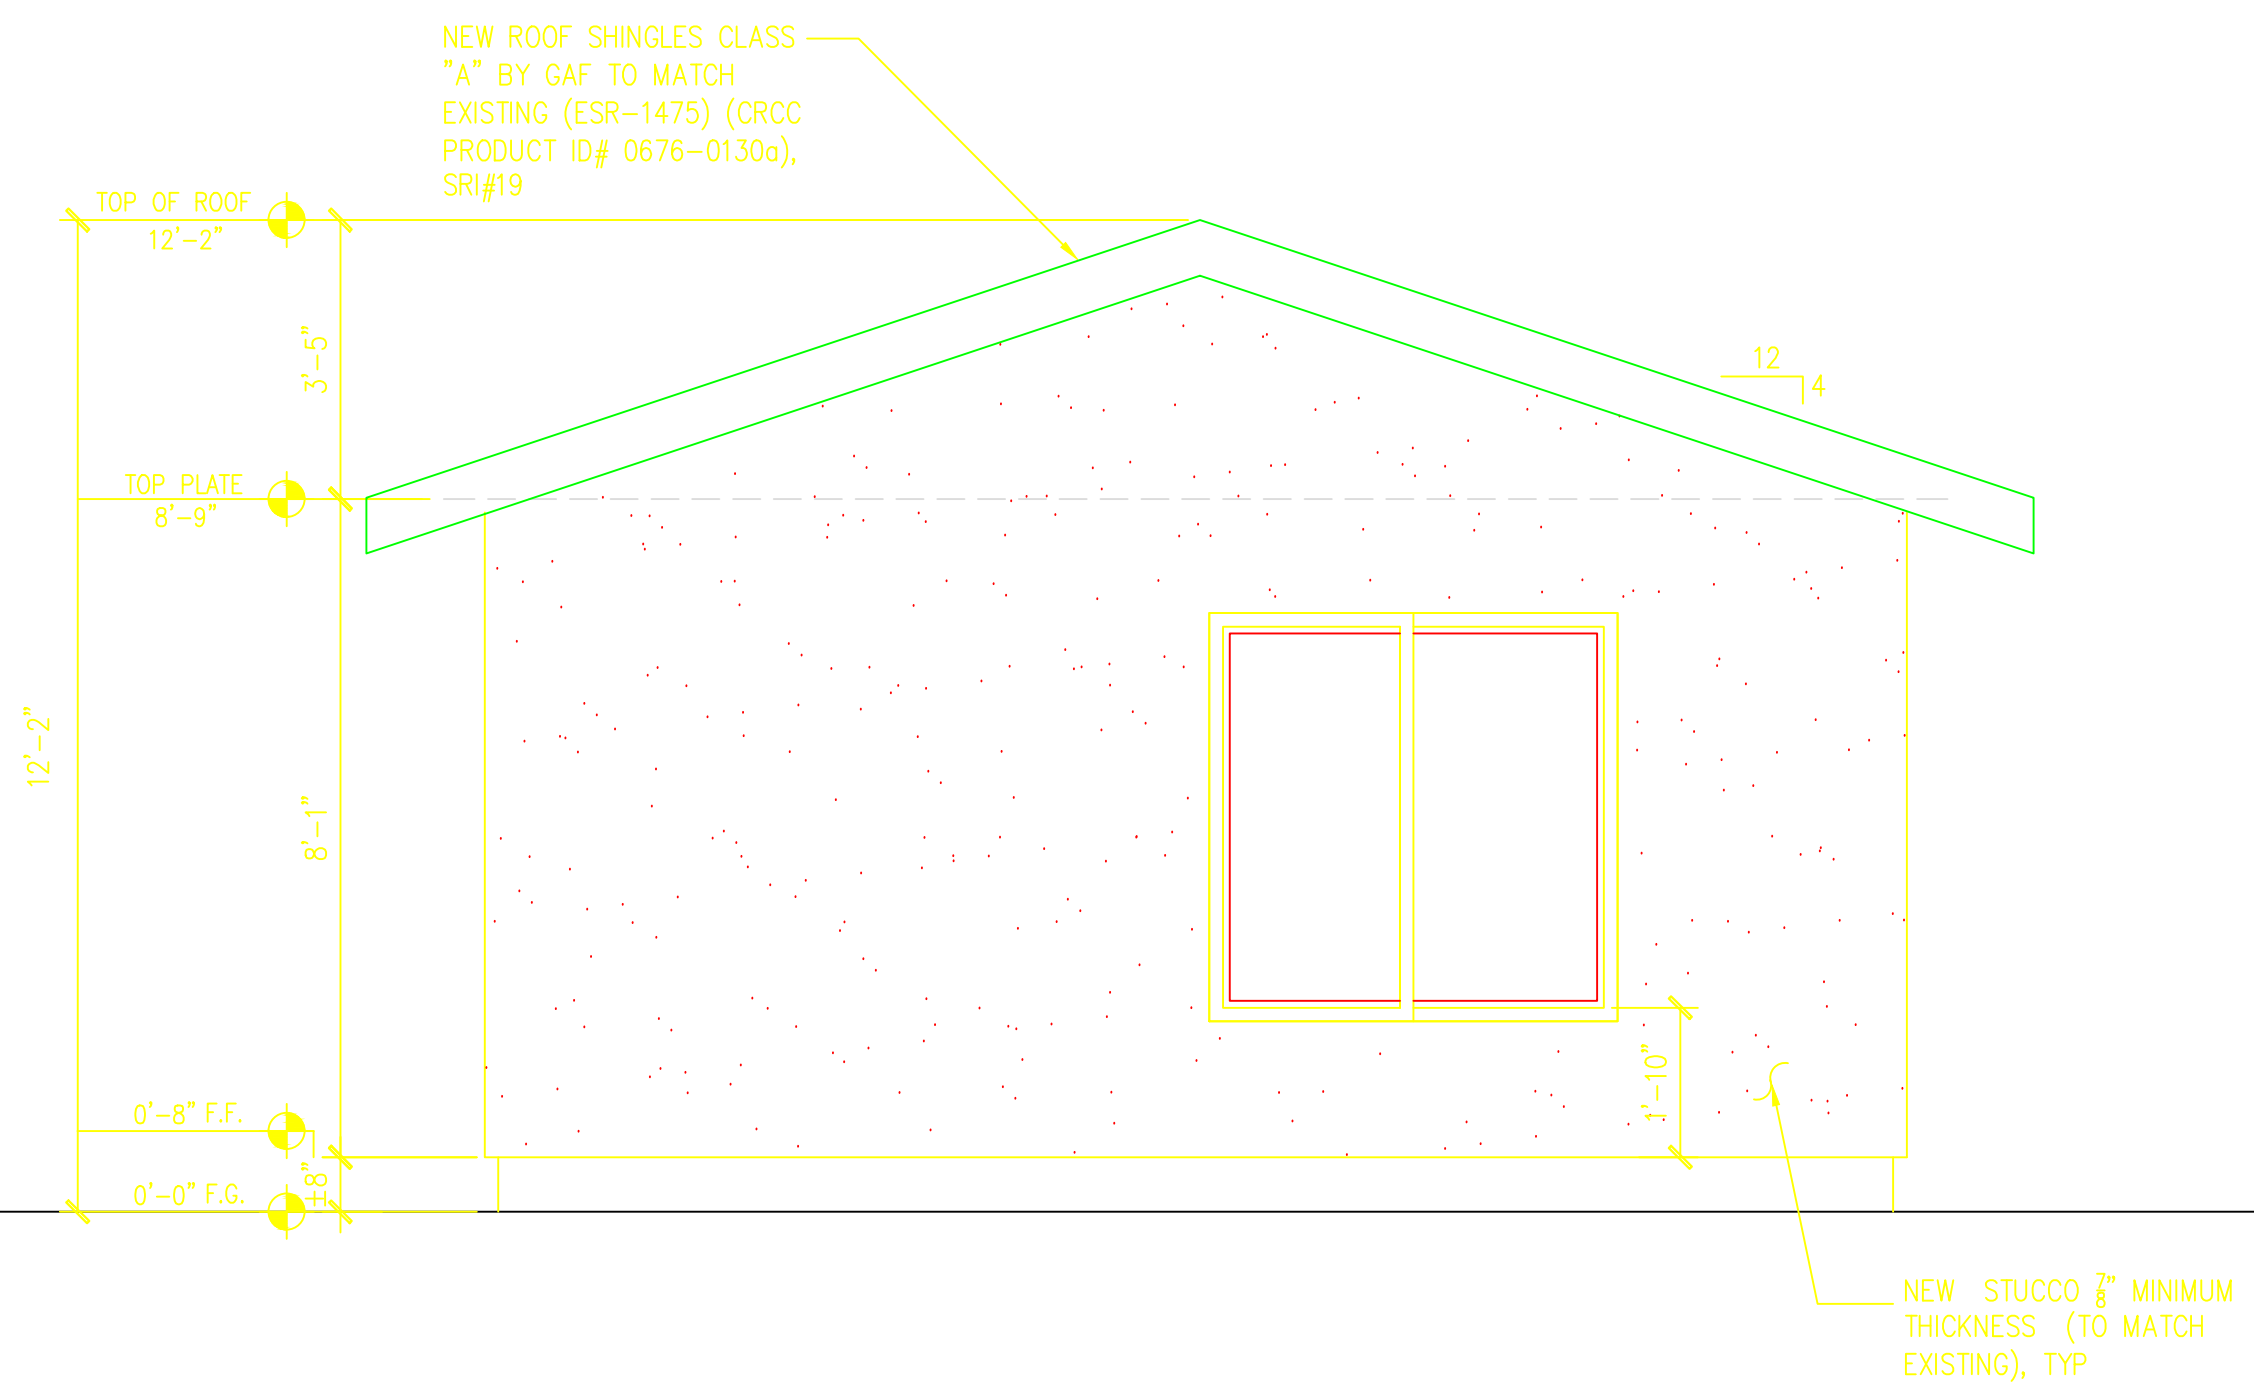

PROPOSED NORTH ELEVATION
3/8 = 1'-0"

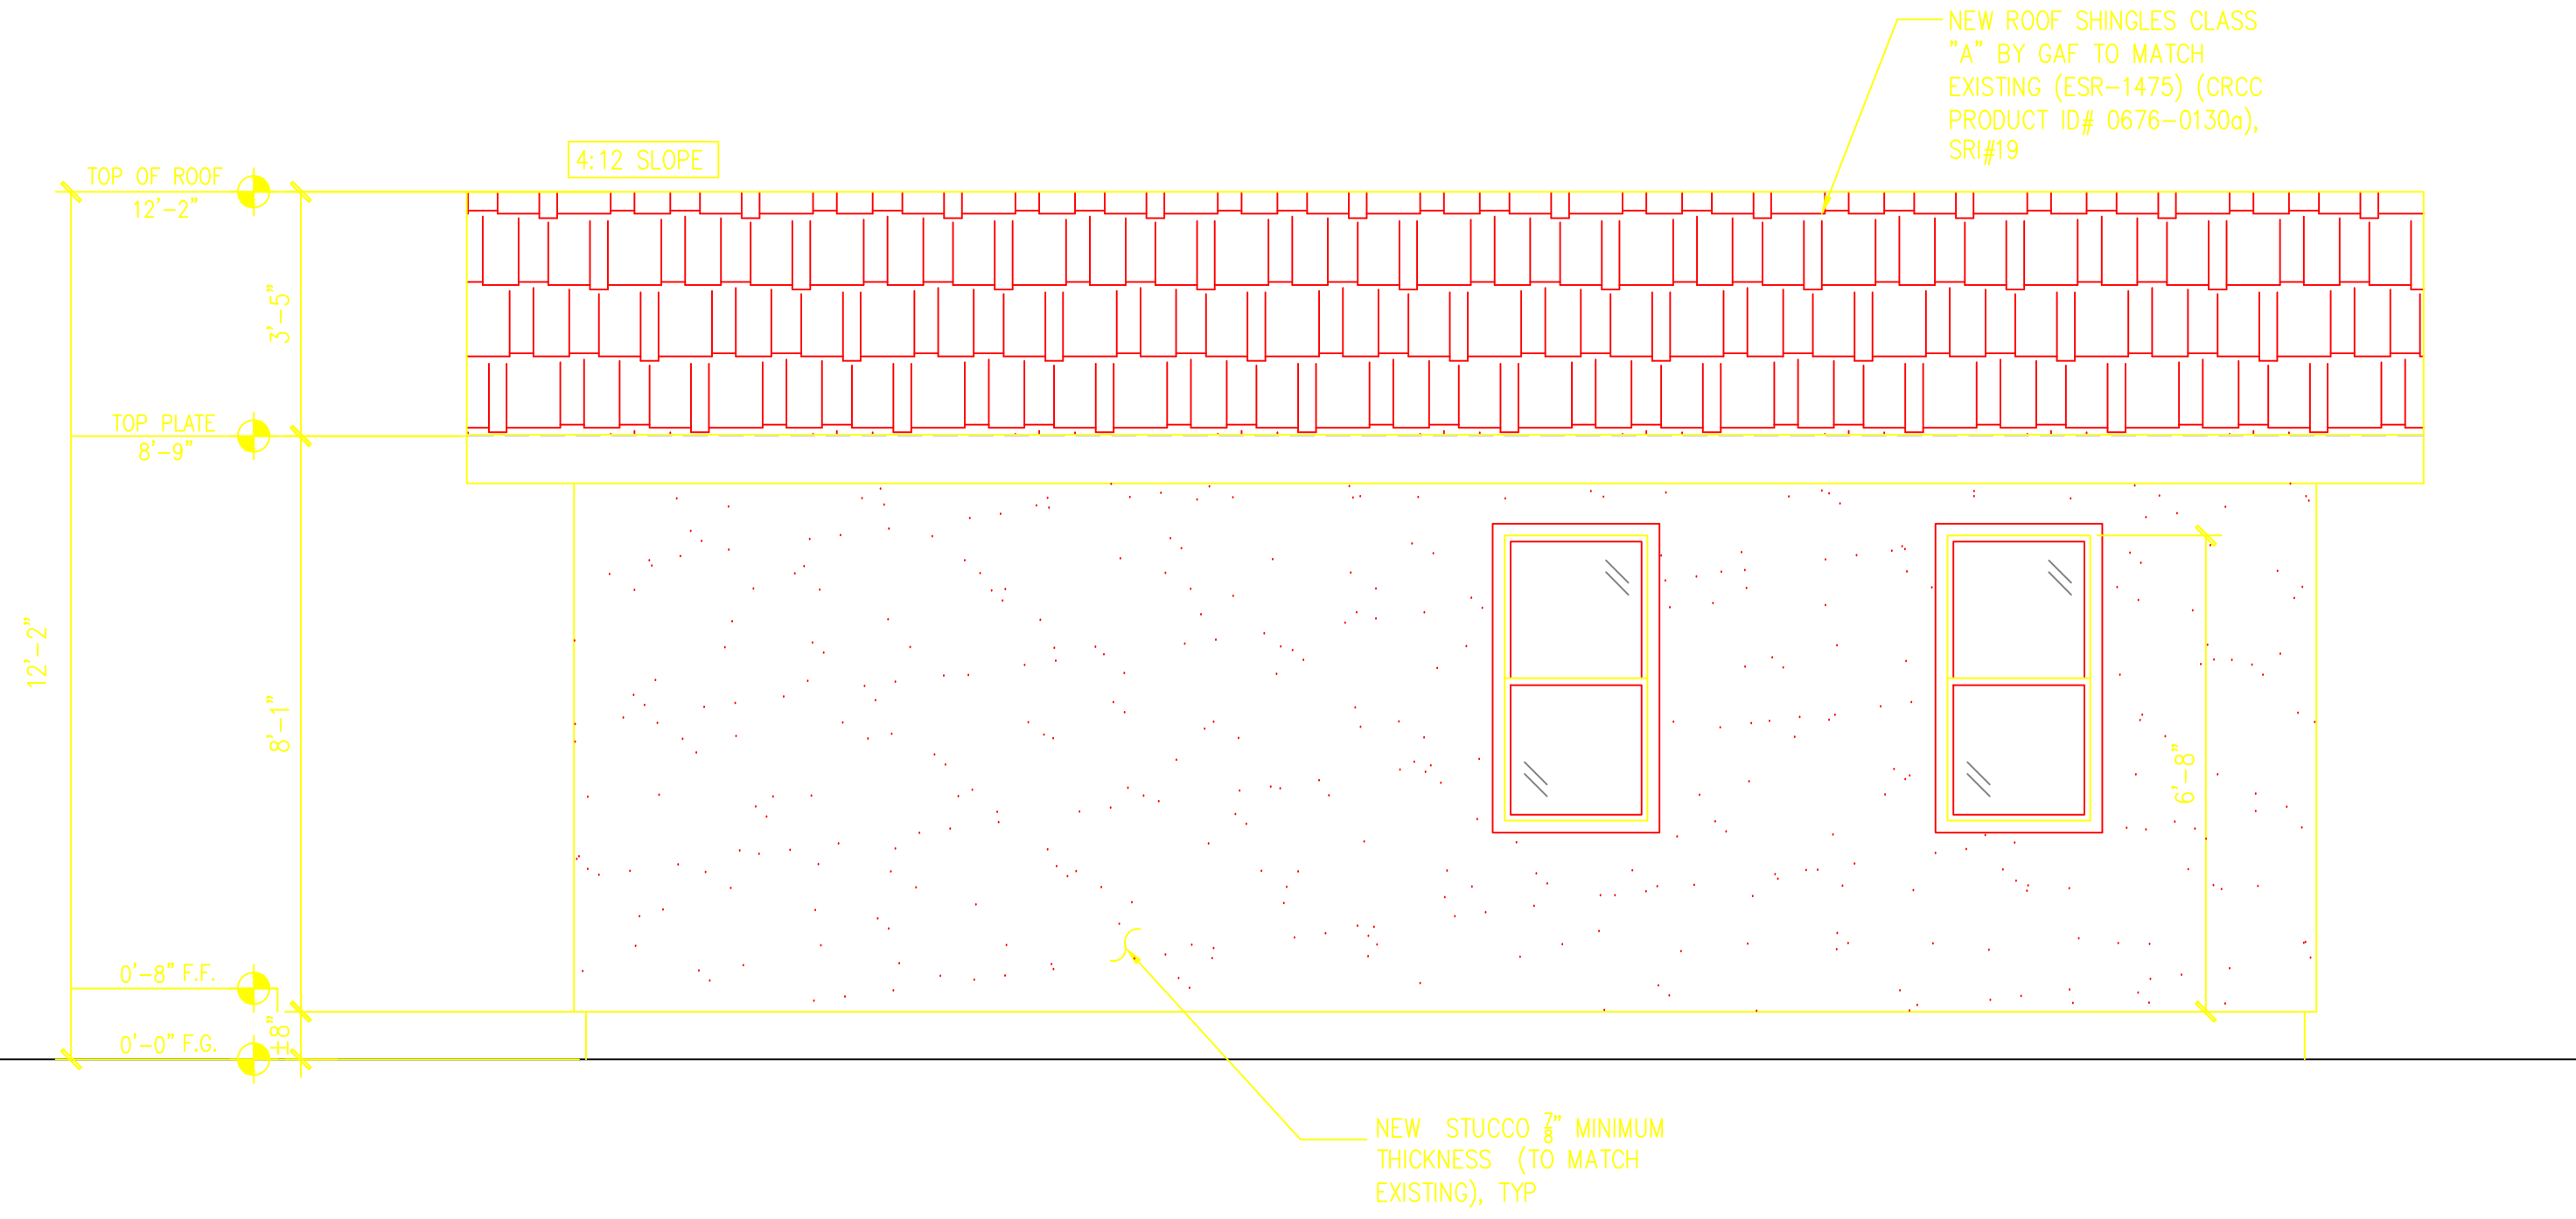

PROPOSED WEST ELEVATION
3/8 = 1'-0"

GENERAL NOTES:

1. CONTRACTOR SHALL VERIFY ALL EXISTING CONDITION AND DIMENSIONS BEFORE ORDERING ANY MATERIALS
2. CONTRACTOR SHALL PROVIDE PROPER SHORING BEFORE ANY DEMOLITION
3. ALL PLANS ARE USED FOR CITY PERMIT ONLY AND SHALL NOT BE USED FOR CONSTRUCTION UNLESS PERMIT IS ISSUED