


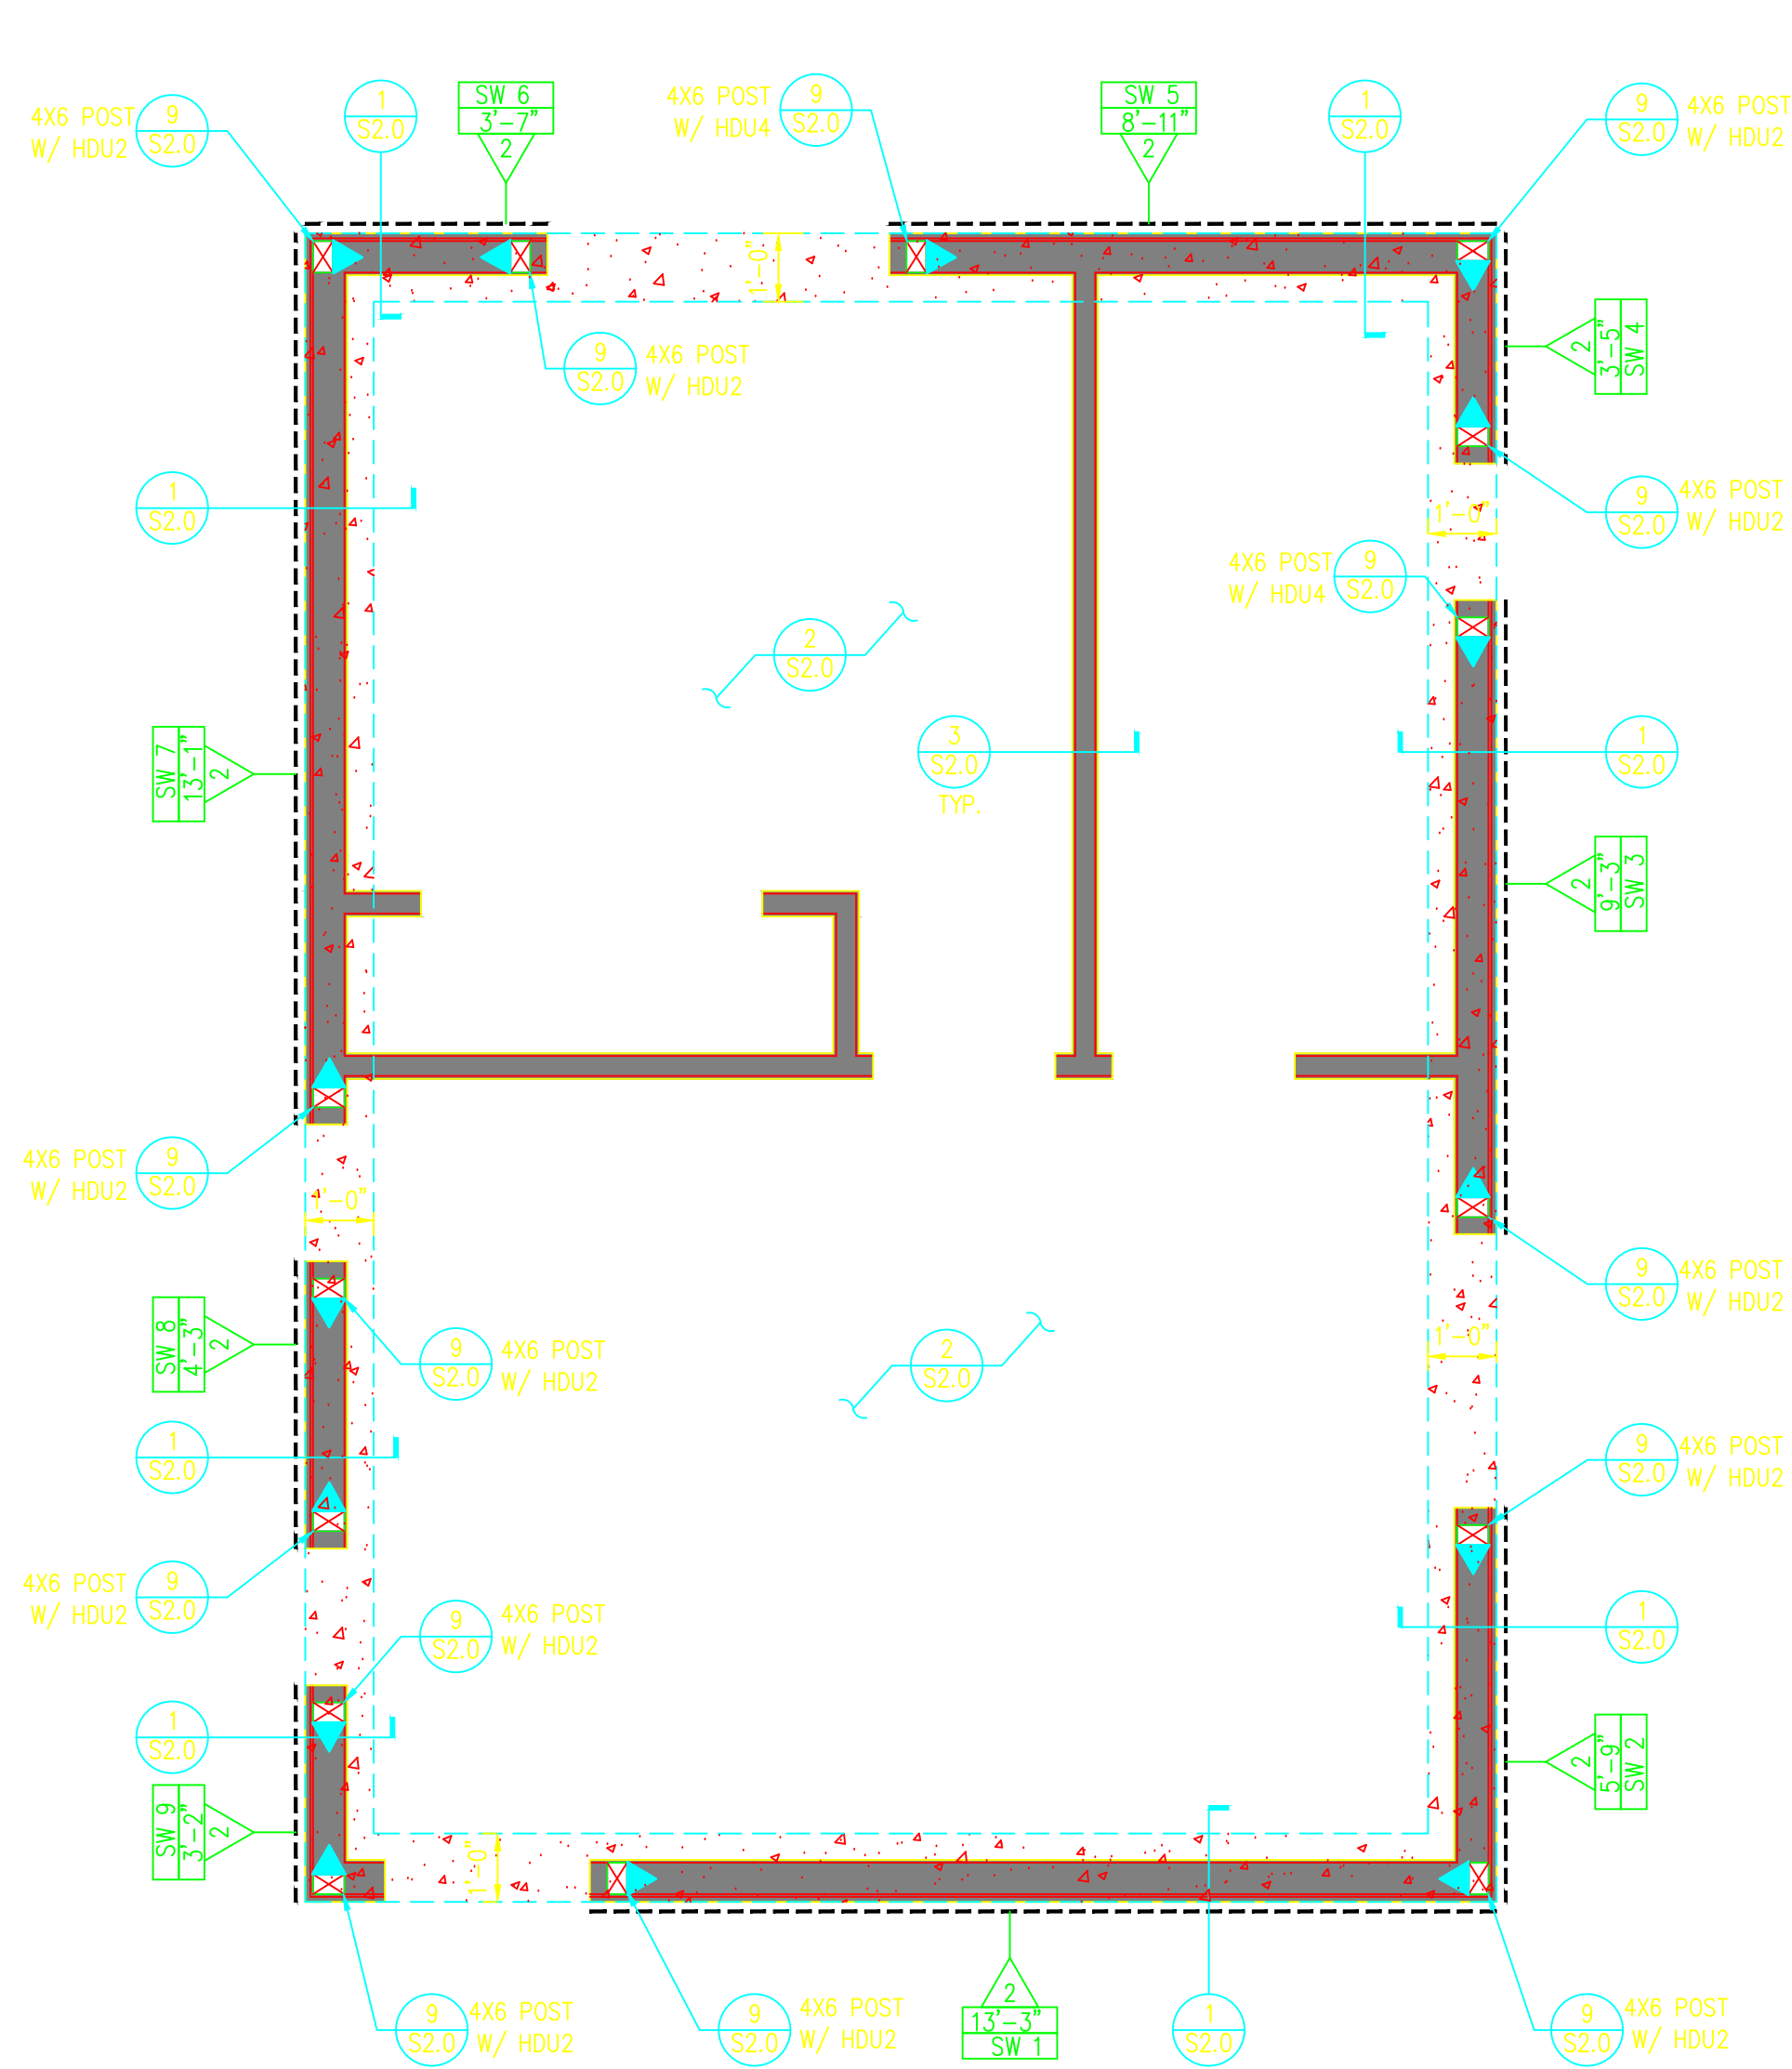


FOUNDATION PLAN
3/8" = 1'-0"

LEGEND:

- 2X6 EXTERIOR STUD WALL
- 2X INTERIOR STUD WALL
- CONTINUOUS FOOTING

PLAN NOTES:

1. FOR GENERAL, AND MATERIAL NOTES, SEE SHEET S0.0
2. FOR SYMBOL LEGEND, AND ABBREVIATION, SEE SHEET S0.0
3. FASTENERS FOR PRESERVATIVE-TREATED OR FIRE-RETARDANT-TREATED WOOD SHALL BE HOT-DIPPED ZINC-COATED GALVANIZED STEEL.
4. ALL PLANS ARE USED FOR CITY PERMIT ONLY AND SHALL NOT BE USED FOR CONSTRUCTION UNLESS PERMIT IS ISSUED
5. CONTRACTOR SHALL VERIFY ALL EXISTING CONDITION AND DIMENSIONS BEFORE ORDERING ANY MATERIALS
6. CONTRACTOR SHALL PROVIDE PROPER SHORING BEFORE ANY DEMOLITION
7. FOR SHEAR WALL ELEVATIONS, SEE SHEET S5.0.
8. FOR SHEAR WALL SCHEDULE, SEE DETAIL 3/S5.0.

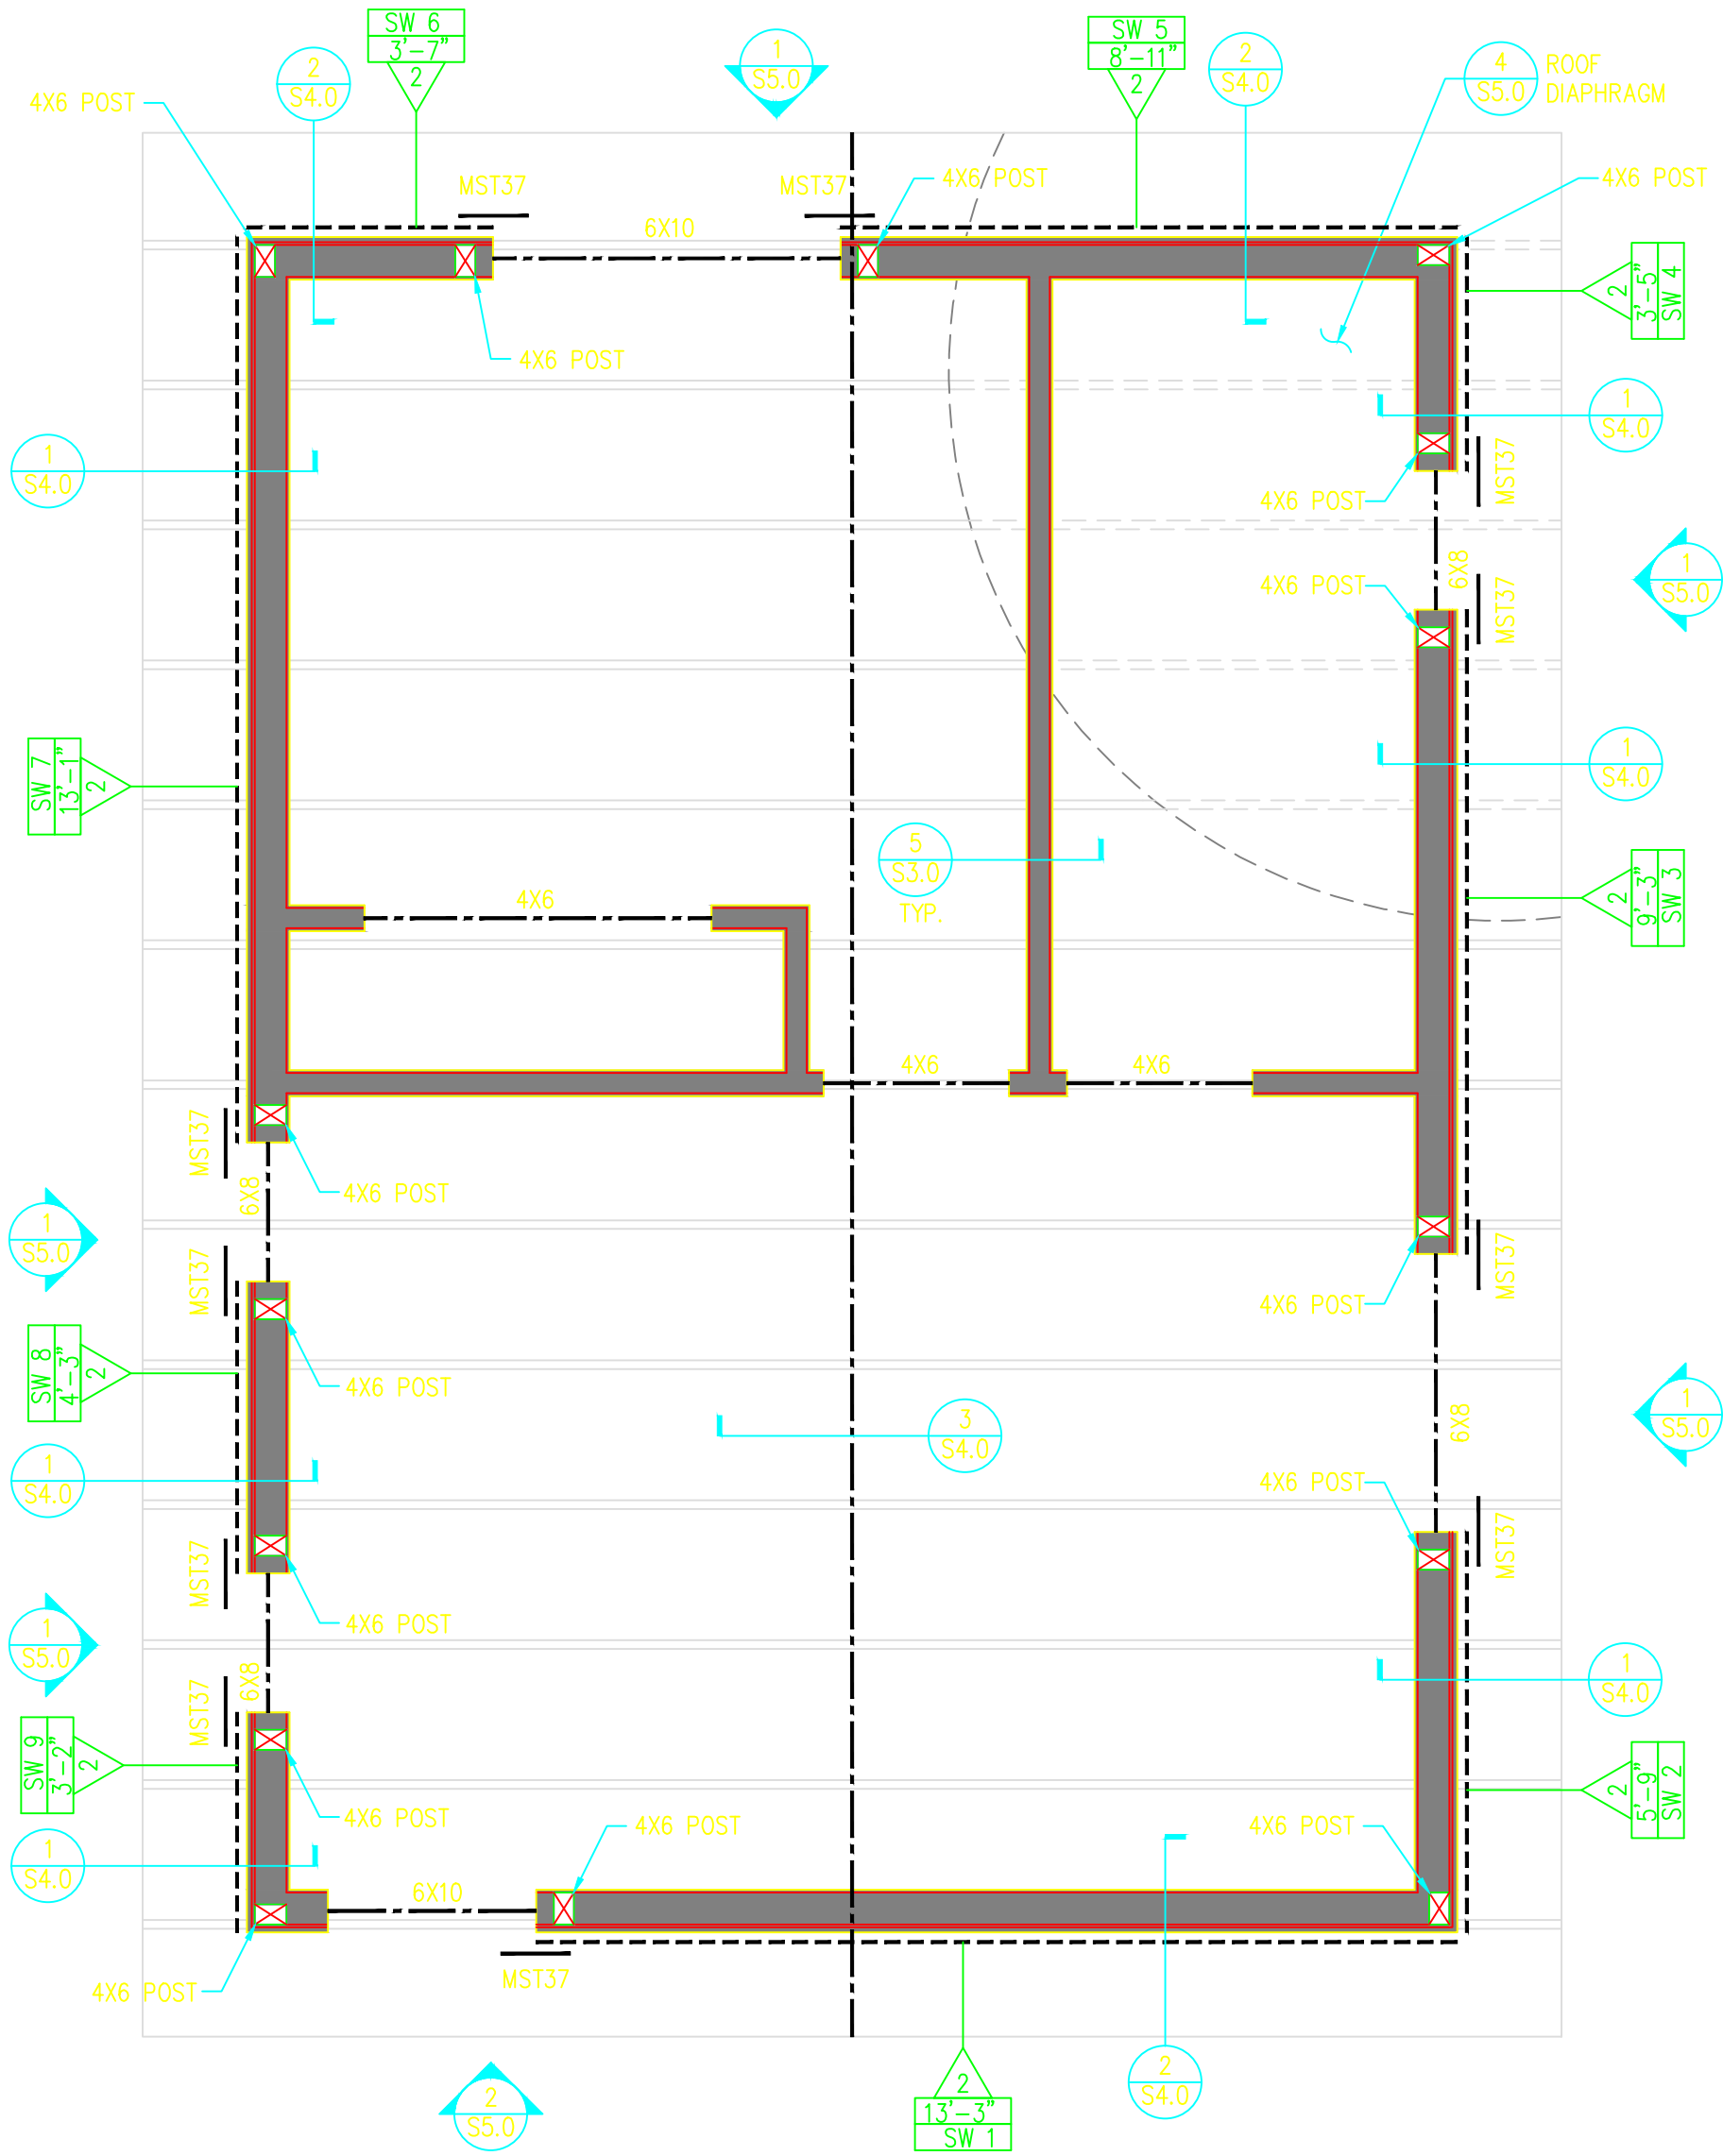

FRAMING PLAN
3/8" = 1'-0"

ROOF TRUSS NOTES:

1. ROOF TRUSSES BY OTHERS.
2. CONTRACTOR SHALL PROVIDE APPLICABLE ROOF TRUSSES LAYOUT, CALCULATIONS, CONNECTION DETAILS AND NECESSARY SUPPORTS TO BUILDING DEPARTMENT FOR APPROVAL PRIOR TO FABRICATION.
3. CONTRACTOR SHALL PROVIDE APPLICABLE ROOF TRUSSES LAYOUT, CALCULATIONS, CONNECTION DETAILS, AND NECESSARY SUPPORTS TO ENGINEER PRIOR TO FABRICATION FOR PLANS COORDINATION.
4. CONTRACTOR SHALL NOT START TRUSSES FABRICATION PRIOR TO CITY PERMIT ISSUANCE.
5. CONTRACTOR SHALL VERIFY ALL CONTROLLING DIMENSIONS AND EXISTING CONDITIONS AND COORDINATE WITH THE ARCHITECTURAL PLANS PRIOR TO FABRICATION.

GENERAL NOTES:

1. CONTRACTOR SHALL VERIFY ALL EXISTING CONDITION AND DIMENSIONS BEFORE ORDERING ANY MATERIALS
2. CONTRACTOR SHALL PROVIDE PROPER SHORING BEFORE ANY DEMOLITION
3. ALL PLANS ARE USED FOR CITY PERMIT ONLY AND SHALL NOT BE USED FOR CONSTRUCTION UNLESS PERMIT IS ISSUED